

DENAH TAPAK

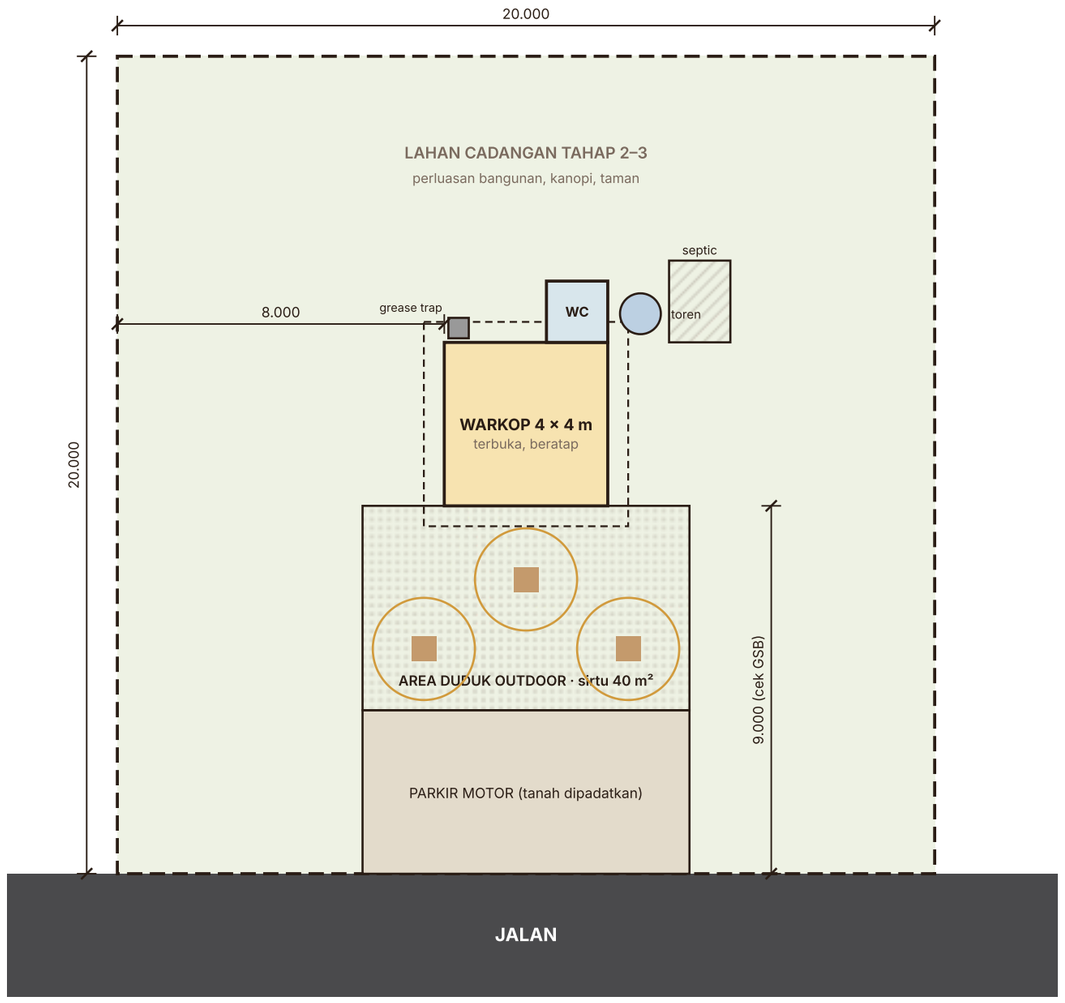

SKALA 1 : 150

DENAH BANGUNAN

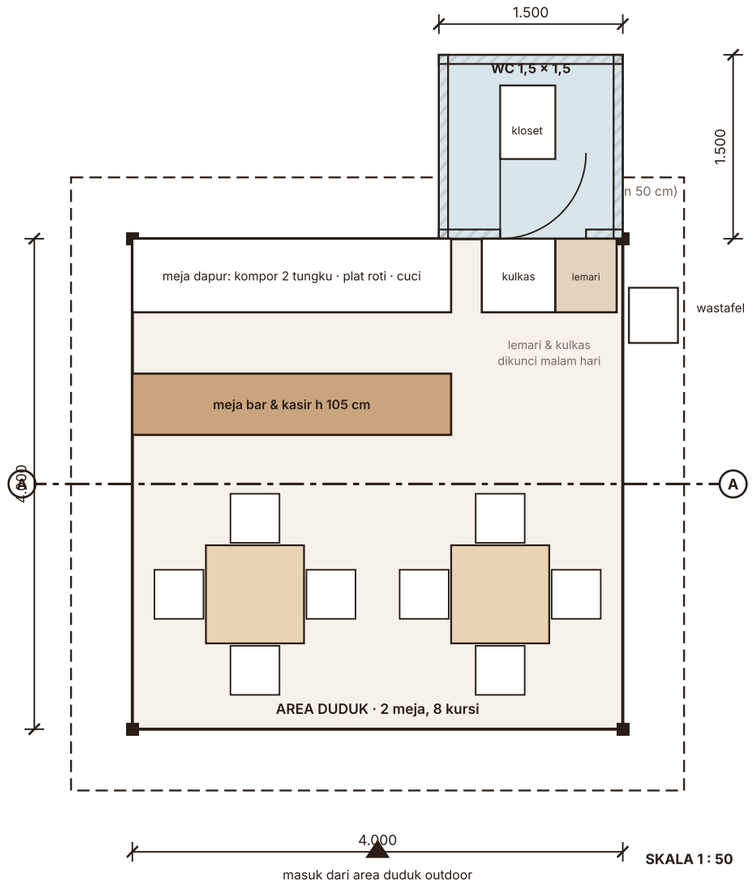

SKALA 1 : 50

RINGKASAN

BANGUNAN BERATAP	TOILET
16 m²	2,25 m²
AREA DUDUK OUTDOOR	**TOTAL BIAYA**
40 m²	Rp 50,0 jt

Konsep


- Warung terbuka beratap 4 × 4 m: bar & dapur di belakang, 2 meja (8 kursi) di bawah atap.
- 3 meja + payung di area duduk outdoor (40 m², sirtu dipadatkan).
- Toilet bata ringan 1,5 × 1,5 m di belakang, toren 550 L di atas dudukan besi.
- Tanpa dinding partisi: kulkas & lemari dikunci di malam hari. Dinding partisi + rolling door masuk Tahap 2.
- Sisa lahan ± 300 m² sebagai cadangan pengembangan.

Catatan


- Ukuran dalam milimeter kecuali disebutkan lain.
- Jarak bangunan dari jalan menyesuaikan garis sempadan bangunan (GSB) setempat.
- Septic tank ≥ 10 m dari sumur (milik sendiri maupun tetangga).



TAMPAK DEPAN · SKALA 1 : 50

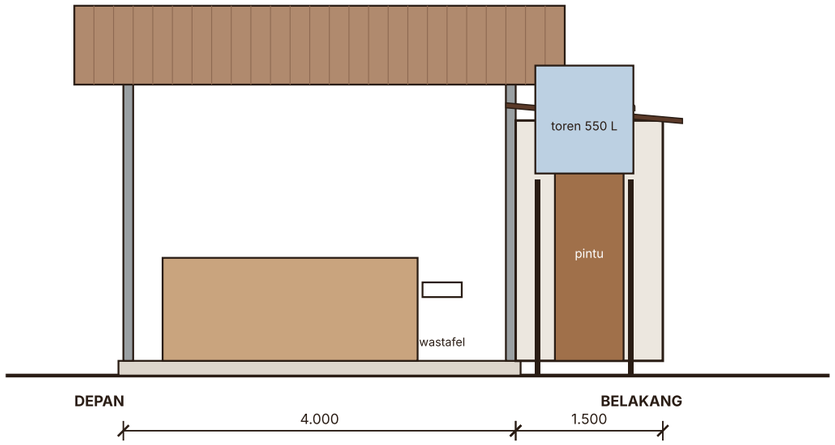

TAMPAK SAMPING KANAN · SKALA 1 : 50

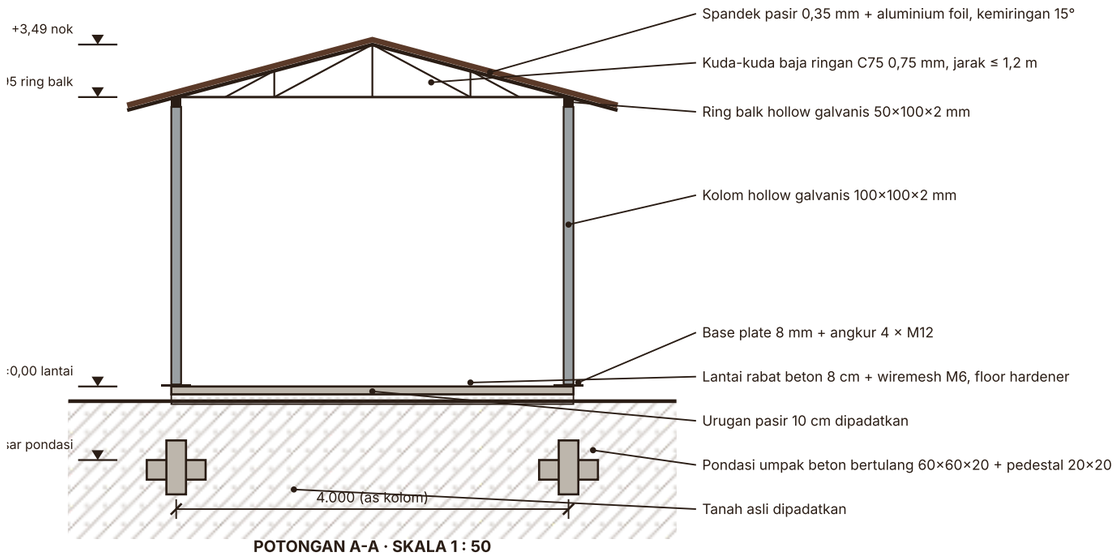

POTONGAN A-A · SKALA 1 : 50

Spesifikasi teknis

- **Struktur:** 4 kolom hollow galvanis 100×100×2 mm, dilas ke base plate 8 mm dengan angkur 4 × M12 ke pondasi umpak.
- **Atap:** pelana 15°, kuda-kuda baja ringan C75 (aplikator bergaransi), penutup spandek pasir 0,35 mm + aluminium foil.
- **Lantai:** rabat beton K-175 tebal 8 cm + wiremesh M6, floor hardener, peil +15 cm dari tanah, miring 1% ke luar.
- **Toilet:** bata ringan 7,5 cm + waterproofing di atas sloof 15×20 cm.
- **Listrik:** 2.200 VA, MCB terpisah untuk dapur, kulkas, dan stop kontak pelanggan; kabel dalam pipa.
- **Air:** dari sumber yang sudah ada (PDAM/sumur) ke toren 550 L. Grease trap sebelum buangan dapur.

Urutan kerja

- Minggu 1: ukur, bowplank, galian & cor pondasi umpak + sloof toilet.
- Minggu 2: septic, pipa, urugan pasir; pasang kolom & ring balk (beton umur ≥ 7 hari).
- Minggu 3: rangka & penutup atap, dinding toilet.
- Minggu 4: lantai rabat + floor hardener, listrik, sanitair, cat, area sirtu.

Gambar ini adalah gambar rencana awal. Minta drafter/insinyur memeriksa ukuran struktur sebelum dipakai untuk PBG dan pelaksanaan.

PERSPEKTIF





Tahap pengembangan (dari laba)

- **Tahap 2** (± Rp 15–20 jt): dinding partisi GRC + rolling door untuk bar & dapur, plafon, lampu teras.
- **Tahap 3** (± Rp 25–35 jt): perluasan atap 4 × 6 m ke depan, area duduk tertutup, Ruang Rembuk.
- **Tahap 4**: paving parkir, pagar, taman.

RENCANA ANGGARAN BIAYA

No	Uraian	Volume	Harga satuan	Jumlah
I	**Persiapan**			**Rp 1.000.000**
	Pembersihan lahan, pengukuran & bowplank	1 ls	Rp 1.000.000	Rp 1.000.000
II	**Pondasi & struktur baja**			**Rp 8.215.000**
	Pondasi umpak beton 60×60 cm + pedestal + angkur	4 titik	Rp 650.000	Rp 2.600.000
	Kolom hollow galvanis 100×100×2 mm (6 m)	4 batang	Rp 520.000	Rp 2.080.000
	Base plate 8 mm + angkur 4 M12 + las	4 titik	Rp 150.000	Rp 600.000
	Ring balk hollow galvanis 50×100×2 mm (6 m)	3 batang	Rp 420.000	Rp 1.260.000
	Upah pasang & las struktur	25 m²	Rp 55.000	Rp 1.375.000
	Cat zinc chromate anti karat	1 ls	Rp 300.000	Rp 300.000
III	**Atap**			**Rp 7.602.000**
	Rangka atap baja ringan C75 + reng	25,9 m²	Rp 165.000	Rp 4.273.500
	Spandek pasir 0,35 mm	25,9 m²	Rp 95.000	Rp 2.460.500
	Aluminium foil 2 sisi	25,9 m²	Rp 20.000	Rp 518.000
	Nok/bubungan	5 m'	Rp 70.000	Rp 350.000
IV	**Lantai & halaman**			**Rp 6.040.000**
	Urugan pasir t = 10 cm	1,6 m³	Rp 300.000	Rp 480.000
	Lantai rabat beton 8 cm + wiremesh M6	16 m²	Rp 180.000	Rp 2.880.000
	Floor hardener	16 m²	Rp 55.000	Rp 880.000
	Area duduk outdoor sirtu dipadatkan	40 m²	Rp 45.000	Rp 1.800.000
V	**Toilet (bata ringan)**			**Rp 8.281.250**
	Sloof beton 15×20 cm	6 m'	Rp 200.000	Rp 1.200.000
	Dinding bata ringan 7,5 cm + plester aci	13 m²	Rp 230.000	Rp 2.990.000
	Lantai rabat toilet	2,25 m²	Rp 180.000	Rp 405.000
	Waterproofing lantai & dinding	11,25 m²	Rp 85.000	Rp 956.250
	Atap toilet (rangka + spandek)	3 m²	Rp 280.000	Rp 840.000
	Pintu PVC + kusen	1 unit	Rp 850.000	Rp 850.000
	Cat dinding toilet	26 m²	Rp 40.000	Rp 1.040.000
VI	**Air & sanitasi**			**Rp 7.000.000**
	Toren 550 L + dudukan besi	1 ls	Rp 1.500.000	Rp 1.500.000
	Instalasi pipa air bersih & kotor	4 titik	Rp 300.000	Rp 1.200.000
	Septic tank buis beton + resapan	1 unit	Rp 2.500.000	Rp 2.500.000
	Kloset jongkok + kran + floor drain	1 unit	Rp 800.000	Rp 800.000
	Wastafel + kran	1 unit	Rp 600.000	Rp 600.000
	Grease trap sederhana	1 unit	Rp 400.000	Rp 400.000
VII	**Listrik**			**Rp 5.940.000**
	Pasang baru PLN 2.200 VA (perkiraan)	1 ls	Rp 2.200.000	Rp 2.200.000
	SLO & NIDI	1 ls	Rp 750.000	Rp 750.000
	Instalasi titik lampu & stop kontak	10 titik	Rp 185.000	Rp 1.850.000
	Panel MCB + grounding	1 ls	Rp 600.000	Rp 600.000
	Lampu LED	6 titik	Rp 90.000	Rp 540.000
VIII	**Perizinan & keselamatan**			**Rp 3.500.000**
	PBG + gambar sederhana (perkiraan)	1 ls	Rp 3.000.000	Rp 3.000.000
	APAR 3 kg	1 unit	Rp 500.000	Rp 500.000
	Jumlah			**Rp 47.578.250**
	Kontingensi 5%			Rp 2.378.912
	TOTAL			**Rp 49.957.162**

Harga perkiraan 2026 (material + upah borongan). Asumsi sumber air sudah ada; sumur bor baru menambah ± Rp 5,5 jt. Kontingensi 5% lebih kecil dari yang disarankan (10%).